GENERAL SHEET NOTES

1. REFER TO SHEET E201 FOR PANEL 'FR1A' LOCATION.
2. REFER TO ARCHITECTURAL ELEVATION FOR LIGHT FIXTURE MOUNTING HEIGHTS.

KEYNOTES

1. REFER TO 2/E701 FOR TYPICAL CLASSROOM LIGHTING CONTROL DIAGRAM.
2. REFER TO 6/E701 FOR INTERIOR LIGHTING CONTROL DIAGRAM.

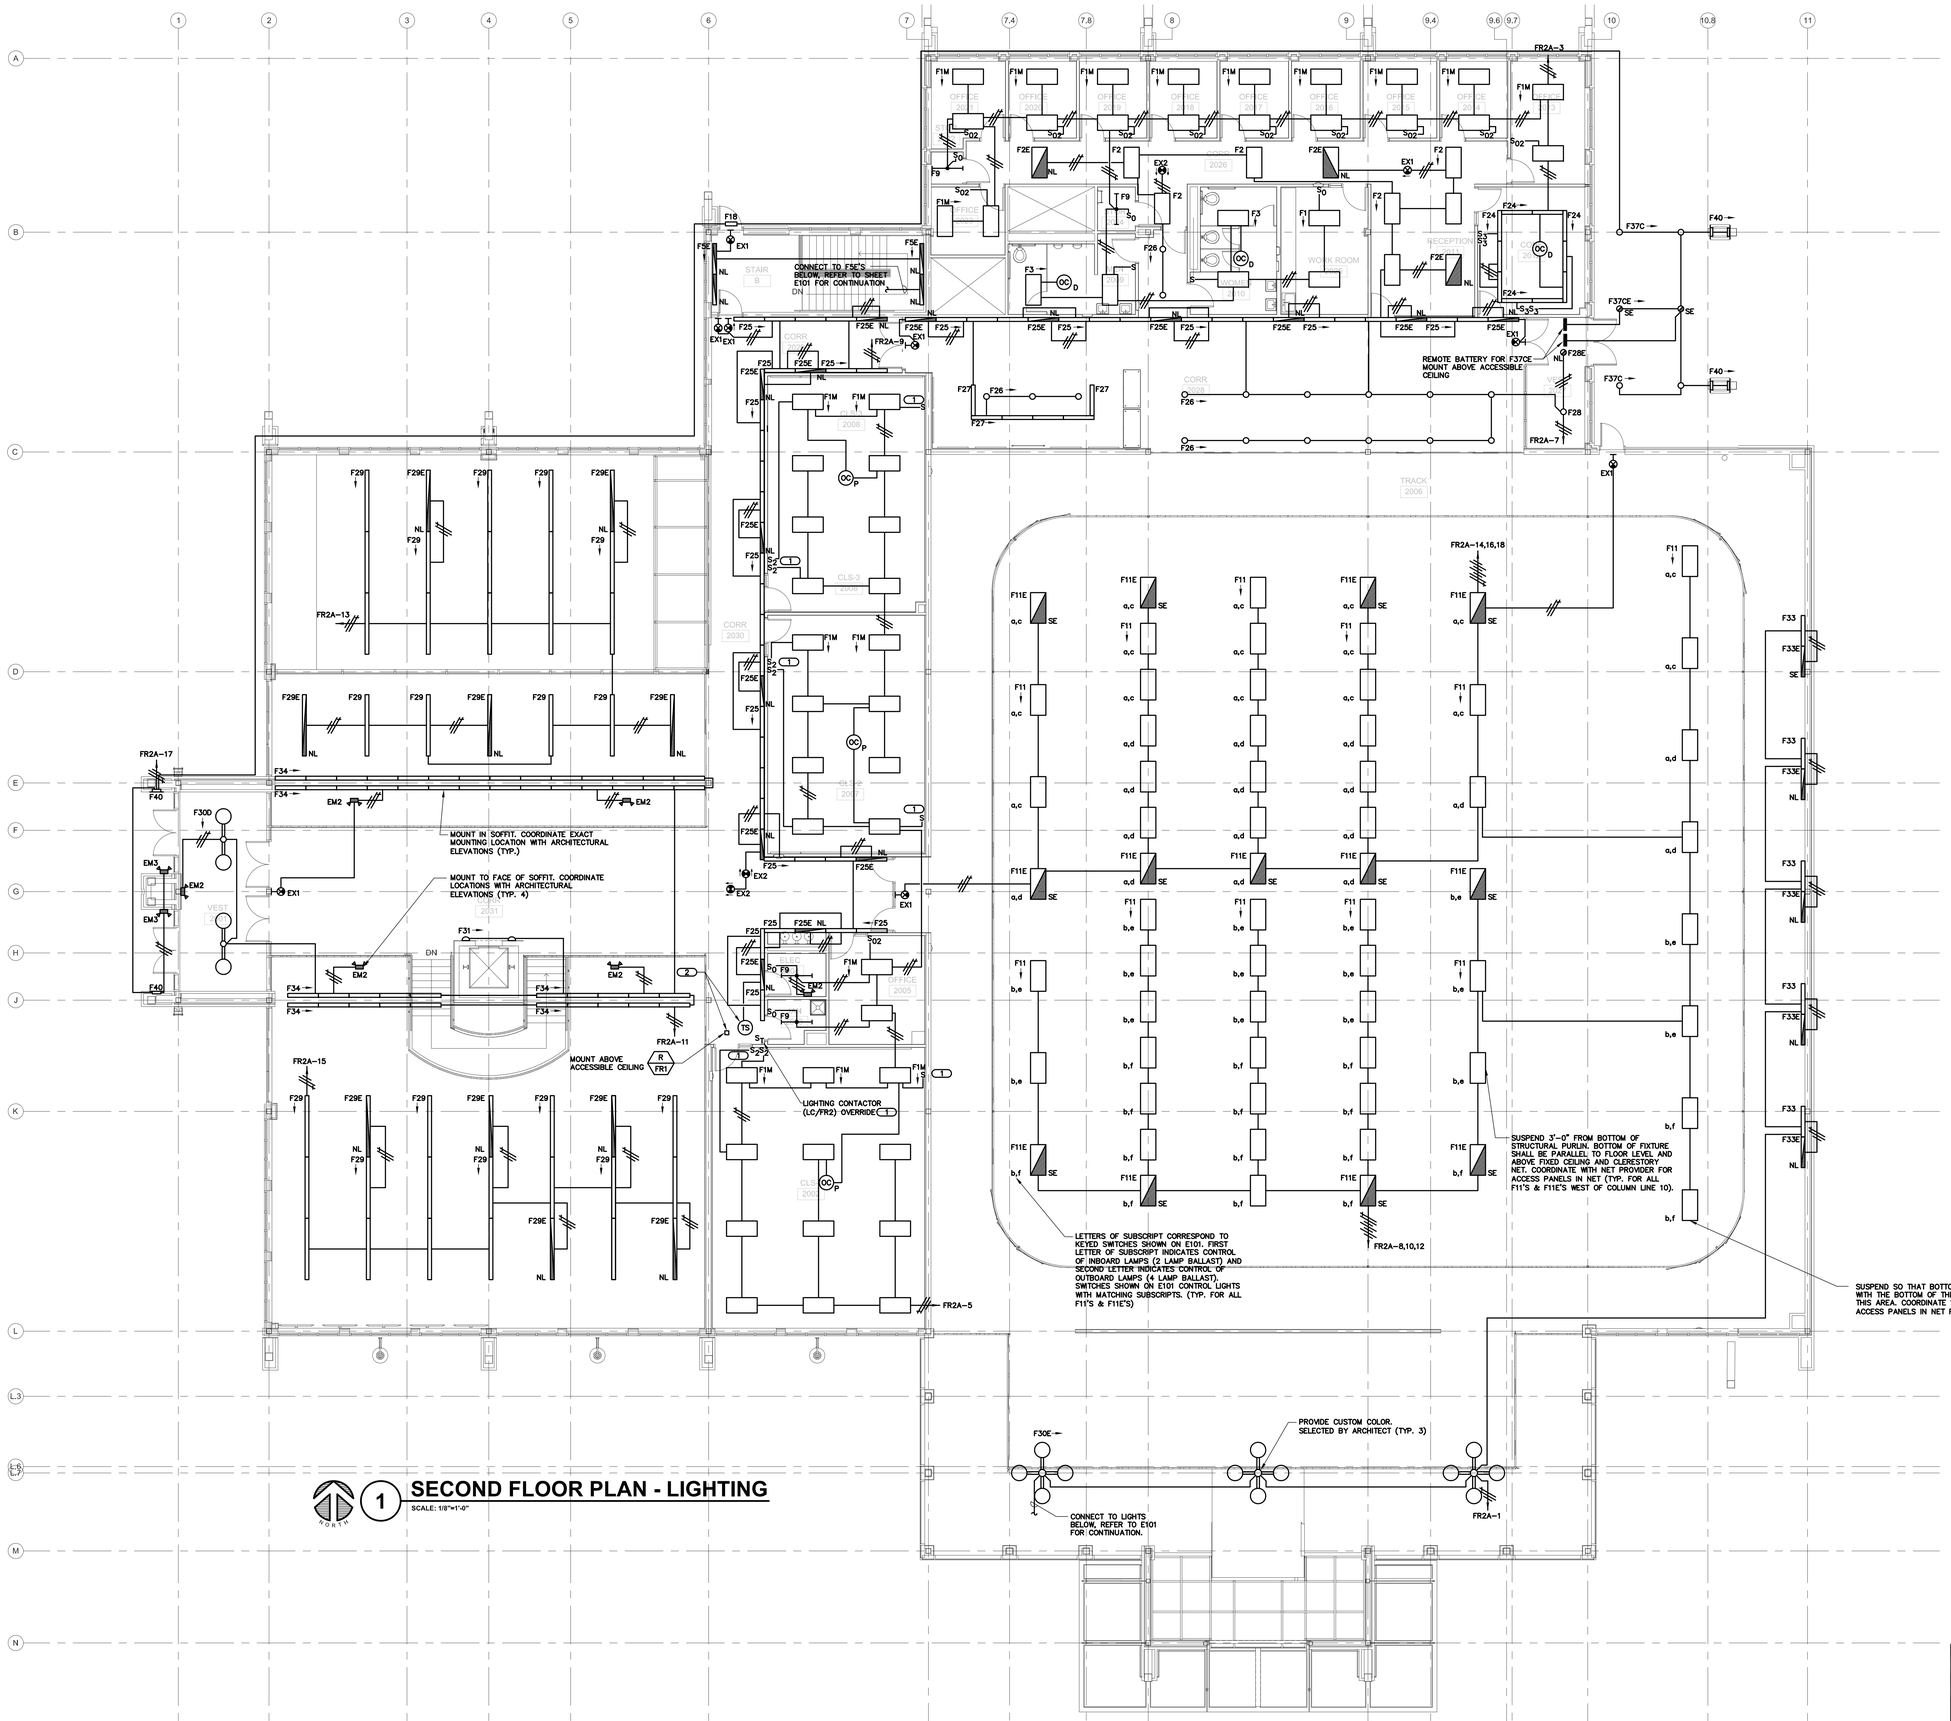

1 **SECOND FLOOR PLAN - LIGHTING**

SCALE: 1/8"=1'-0"

KJWW ENGINEERING CONSULTANTS
Experience you can build on.™
623 26TH AVENUE
ROCK ISLAND, ILLINOIS 61201
309.788.0673
FAX: 309.786.5967
www.kjww.com
STRUCTURAL : MECHANICAL : ELECTRICAL : TECHNOLOGY

date 12/03/07
revised
FOR CONSTRUCTION 3/13/08

drawn by CRG
checked by MEW/LVO

BLDD ARCHITECTS
BLDD Architects, Inc.
201 East Grove Street
Bloomington, Illinois 61701
Phone: 309-828-5025
Fax: 309-828-5127

Design Firm Registration #184-000723

COPYRIGHT 2007 BY BLDD ARCHITECTS, INC.
All rights reserved. No part of this document may be reproduced or transmitted in any form or by any means, electronic or mechanical, including photocopying, recording, or by any information or storage retrieval system, without the written permission of the author, except where by permitted by law.

SECOND FLOOR PLAN - LIGHTING

Phase II Campus Project
Fitness & Rec Center
Heartland Community College
1500 W. Raab Rd, Normal, IL

KJWW ENGINEERING CONSULTANTS
623 26th AVENUE
ROCK ISLAND, IL 61201
309.788.0673 FAX: 309.786.5967
www.kjww.com
Experience you can build on.™
PROJECT #07.0178.04

KJWW ENGINEERING RESERVES PROPRIETARY RIGHTS, INCLUDING COPYRIGHTS, TO THIS DRAWING AND THE DATA SHOWN THEREON. SAID DRAWING AND/OR DATA ARE THE EXCLUSIVE PROPERTY OF KJWW ENGINEERING AND SHALL NOT BE USED OR REPRODUCED FOR ANY OTHER PROJECT WITHOUT THE EXPRESS WRITTEN APPROVAL AND PARTICIPATION OF KJWW ENGINEERING. © 2007 KJWW, P.C.

REFERENCE SCALE IN INCHES 0 1 2 3

sheet
E102

project 061069.404

E102.dwg 0'-1" 10/18/2007 4:27 P.M. By:rosalespr

FOR CONSTRUCTION